
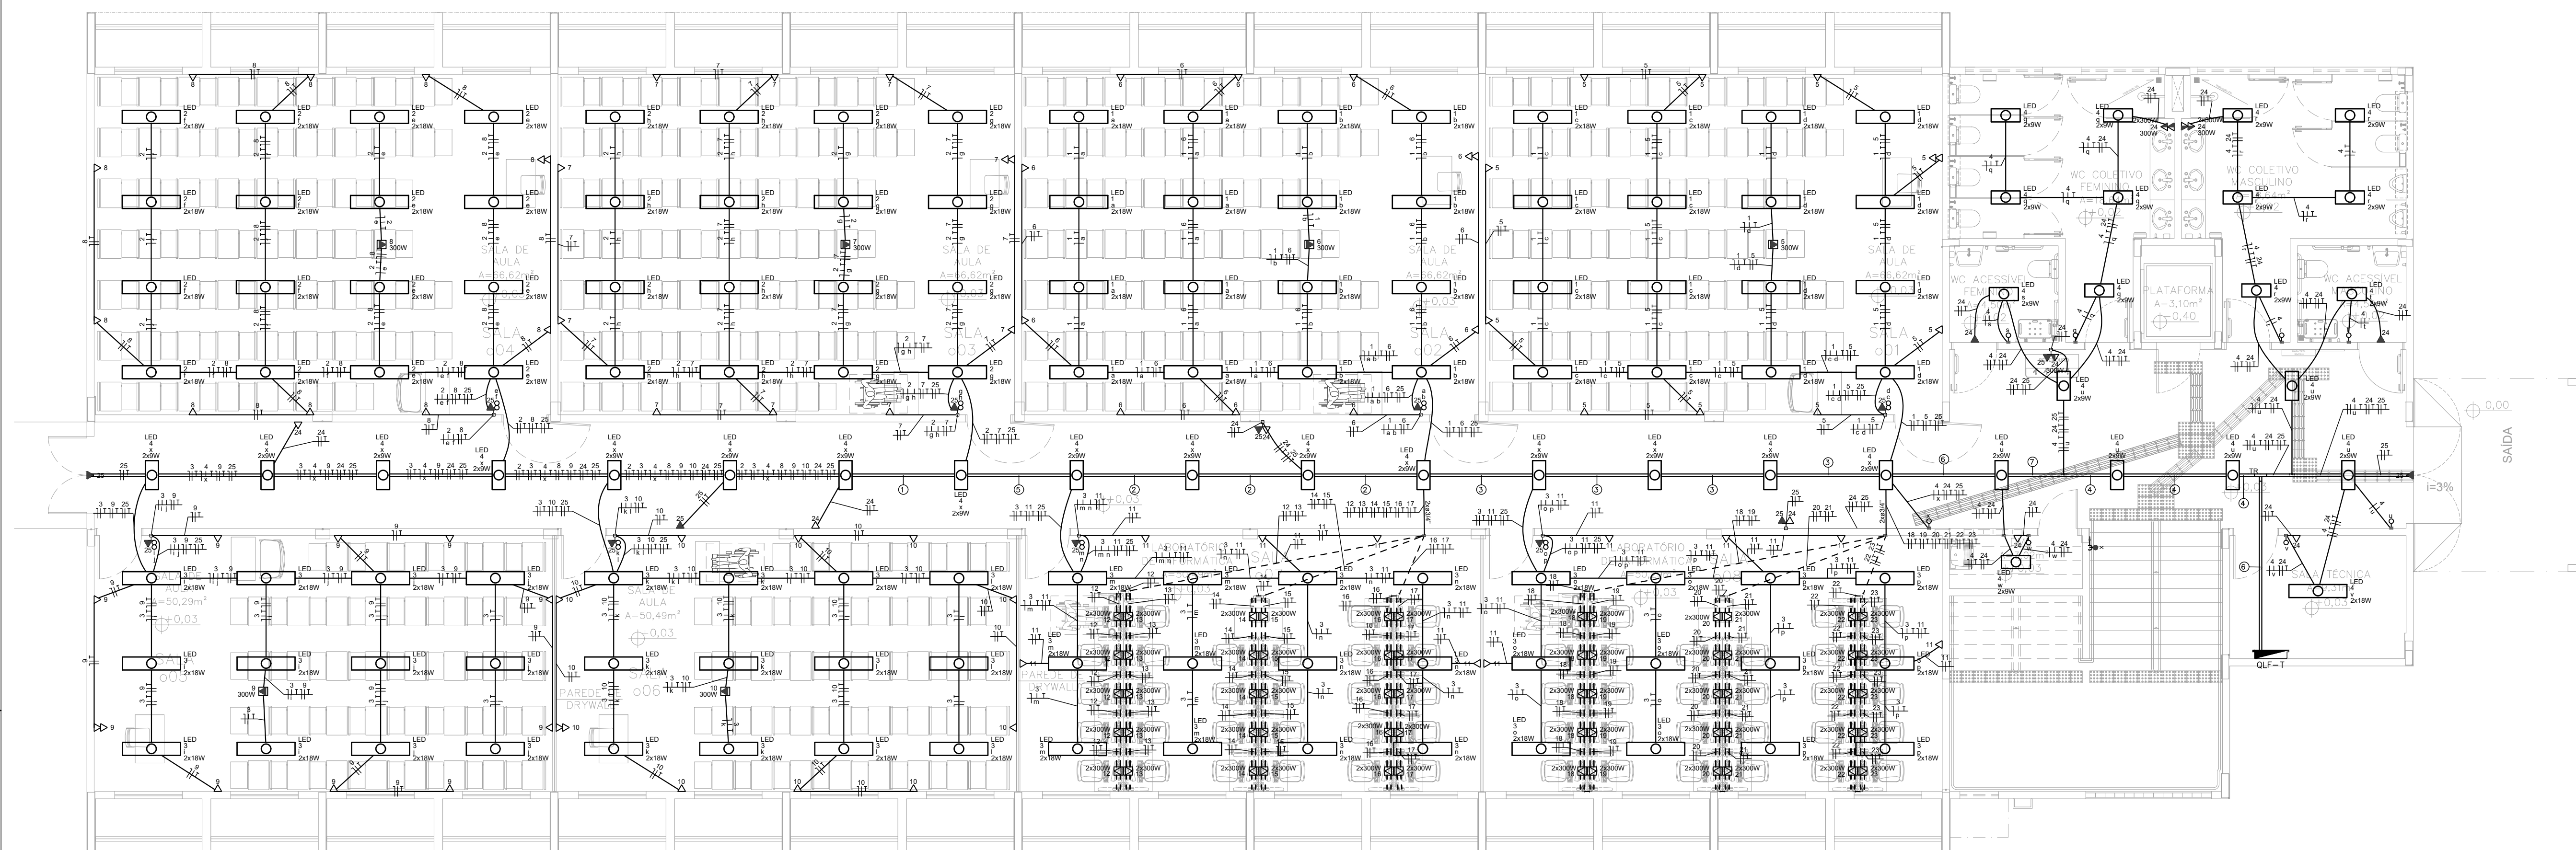


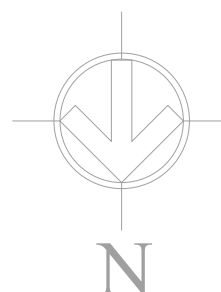

1 PROJETO ELÉTRICO DE FORÇA E LUZ - TÉRREO
1:75

Legenda de condutos - Térreo e superior	
Elétrica	
—	Eletroduto de pvc, 3/4", embutido no forro ou parede
- - - - -	Eletroduto de pvc, 3/4", embutido no piso
=====	Eletrocabla de aço galvanizado, 50x50 mm, embutido no forro
=====	Canaleta evolutiva

Legenda - Térreo	
	2 Tomadas baixas a 0,30m do piso
	2 Tomadas médias a 1,10m do piso
	Caixa 2x4" de embutir
	Caixa de passagem 300x300x300 no piso
	Entrada de serviço
	Interruptor paralelo 1 tecla - 1,10m do piso
	Interruptor simples 1 tecla - 1,10m do piso
	Interruptor simples 2 teclas - 1,10m do piso
	Lâmpada LED
	Quadro de distribuição
	Quadro de medição
	Saída horizontal para eletroduto T reto 90°
	Tomada alta a 2,20m do piso
	Tomada alta a 2,80m do piso
	Tomada baixa a 0,30m do piso
	Tomada média a 1,10m do piso
	Tomada no piso

Legenda do Faço - Térreo									
①	2	3	4	8	9	10			
	24	25							
②	2	3	4	7	8	9			
	10	11	24	25					
⑤	1	2	3	4	6	7			
	8	9	10	11	12	13			
	14	15	16	17	24	25			
④	1	2	3	4	5	6			
	7	8	9	10	11	12			
	13	14	15	16	17	18			
	19	20	21	22	23	24			
	25								
⑤	2	3	4	7	8	9			
	10	24	25						
⑥	1	2	3	4	5	6			
	7	8	9	10	11	12			
	13	14	15	16	17	18			
	19	20	21	22	23	24			
	25								
⑦	1	2	3	4	5	6			
	7	8	9	10	11	12			
	13	14	15	16	17	18			
	19	20	21	22	23	24			
	25								

PROJETO DE INSTALAÇÕES ELÉTRICAS

RESPONSÁVEL TÉCNICO:

André Wagner de Barros Silva, Engenheiro Eletricista
CREA-CE 06118048-2
ART nº CE20241547192

UNIVERSIDADE FEDERAL DO CARIRI - UFCA

PROPRIETÁRIO

Av. Ten. Raimundo Rocha, Nº 1639 - Cidade Universitária
Juazeiro do Norte - CE, CEP: 63048-080

ENDEREÇO DA EDIFICAÇÃO

23507.004014/2024-82

NÚMERO DO PROCESSO

ÁREA CONSTRUÍDA

TAXA DE OCUPAÇÃO

COEFICIENTE DE APROVEITAMENTO

CLIENTE / PROJETO

PROJETO DE INSTALAÇÕES ELÉTRICAS DE BAIXA TENSÃO

PROJETO DE INSTALAÇÕES ELÉTRICAS - BLOCO O

DESENHOS DA PRANCHA

PROJETO ELÉTRICO DE FORÇA E LUZ - TÉRREO

ESCALA

1:75

ETAPA

PROJETO EXECUTIVO

RESPONSÁVEL - DESENHO

ANDRÉ WAGNER

REVISÃO

00

DATA

JANEIRO 2025

PRANCHA 01/03